



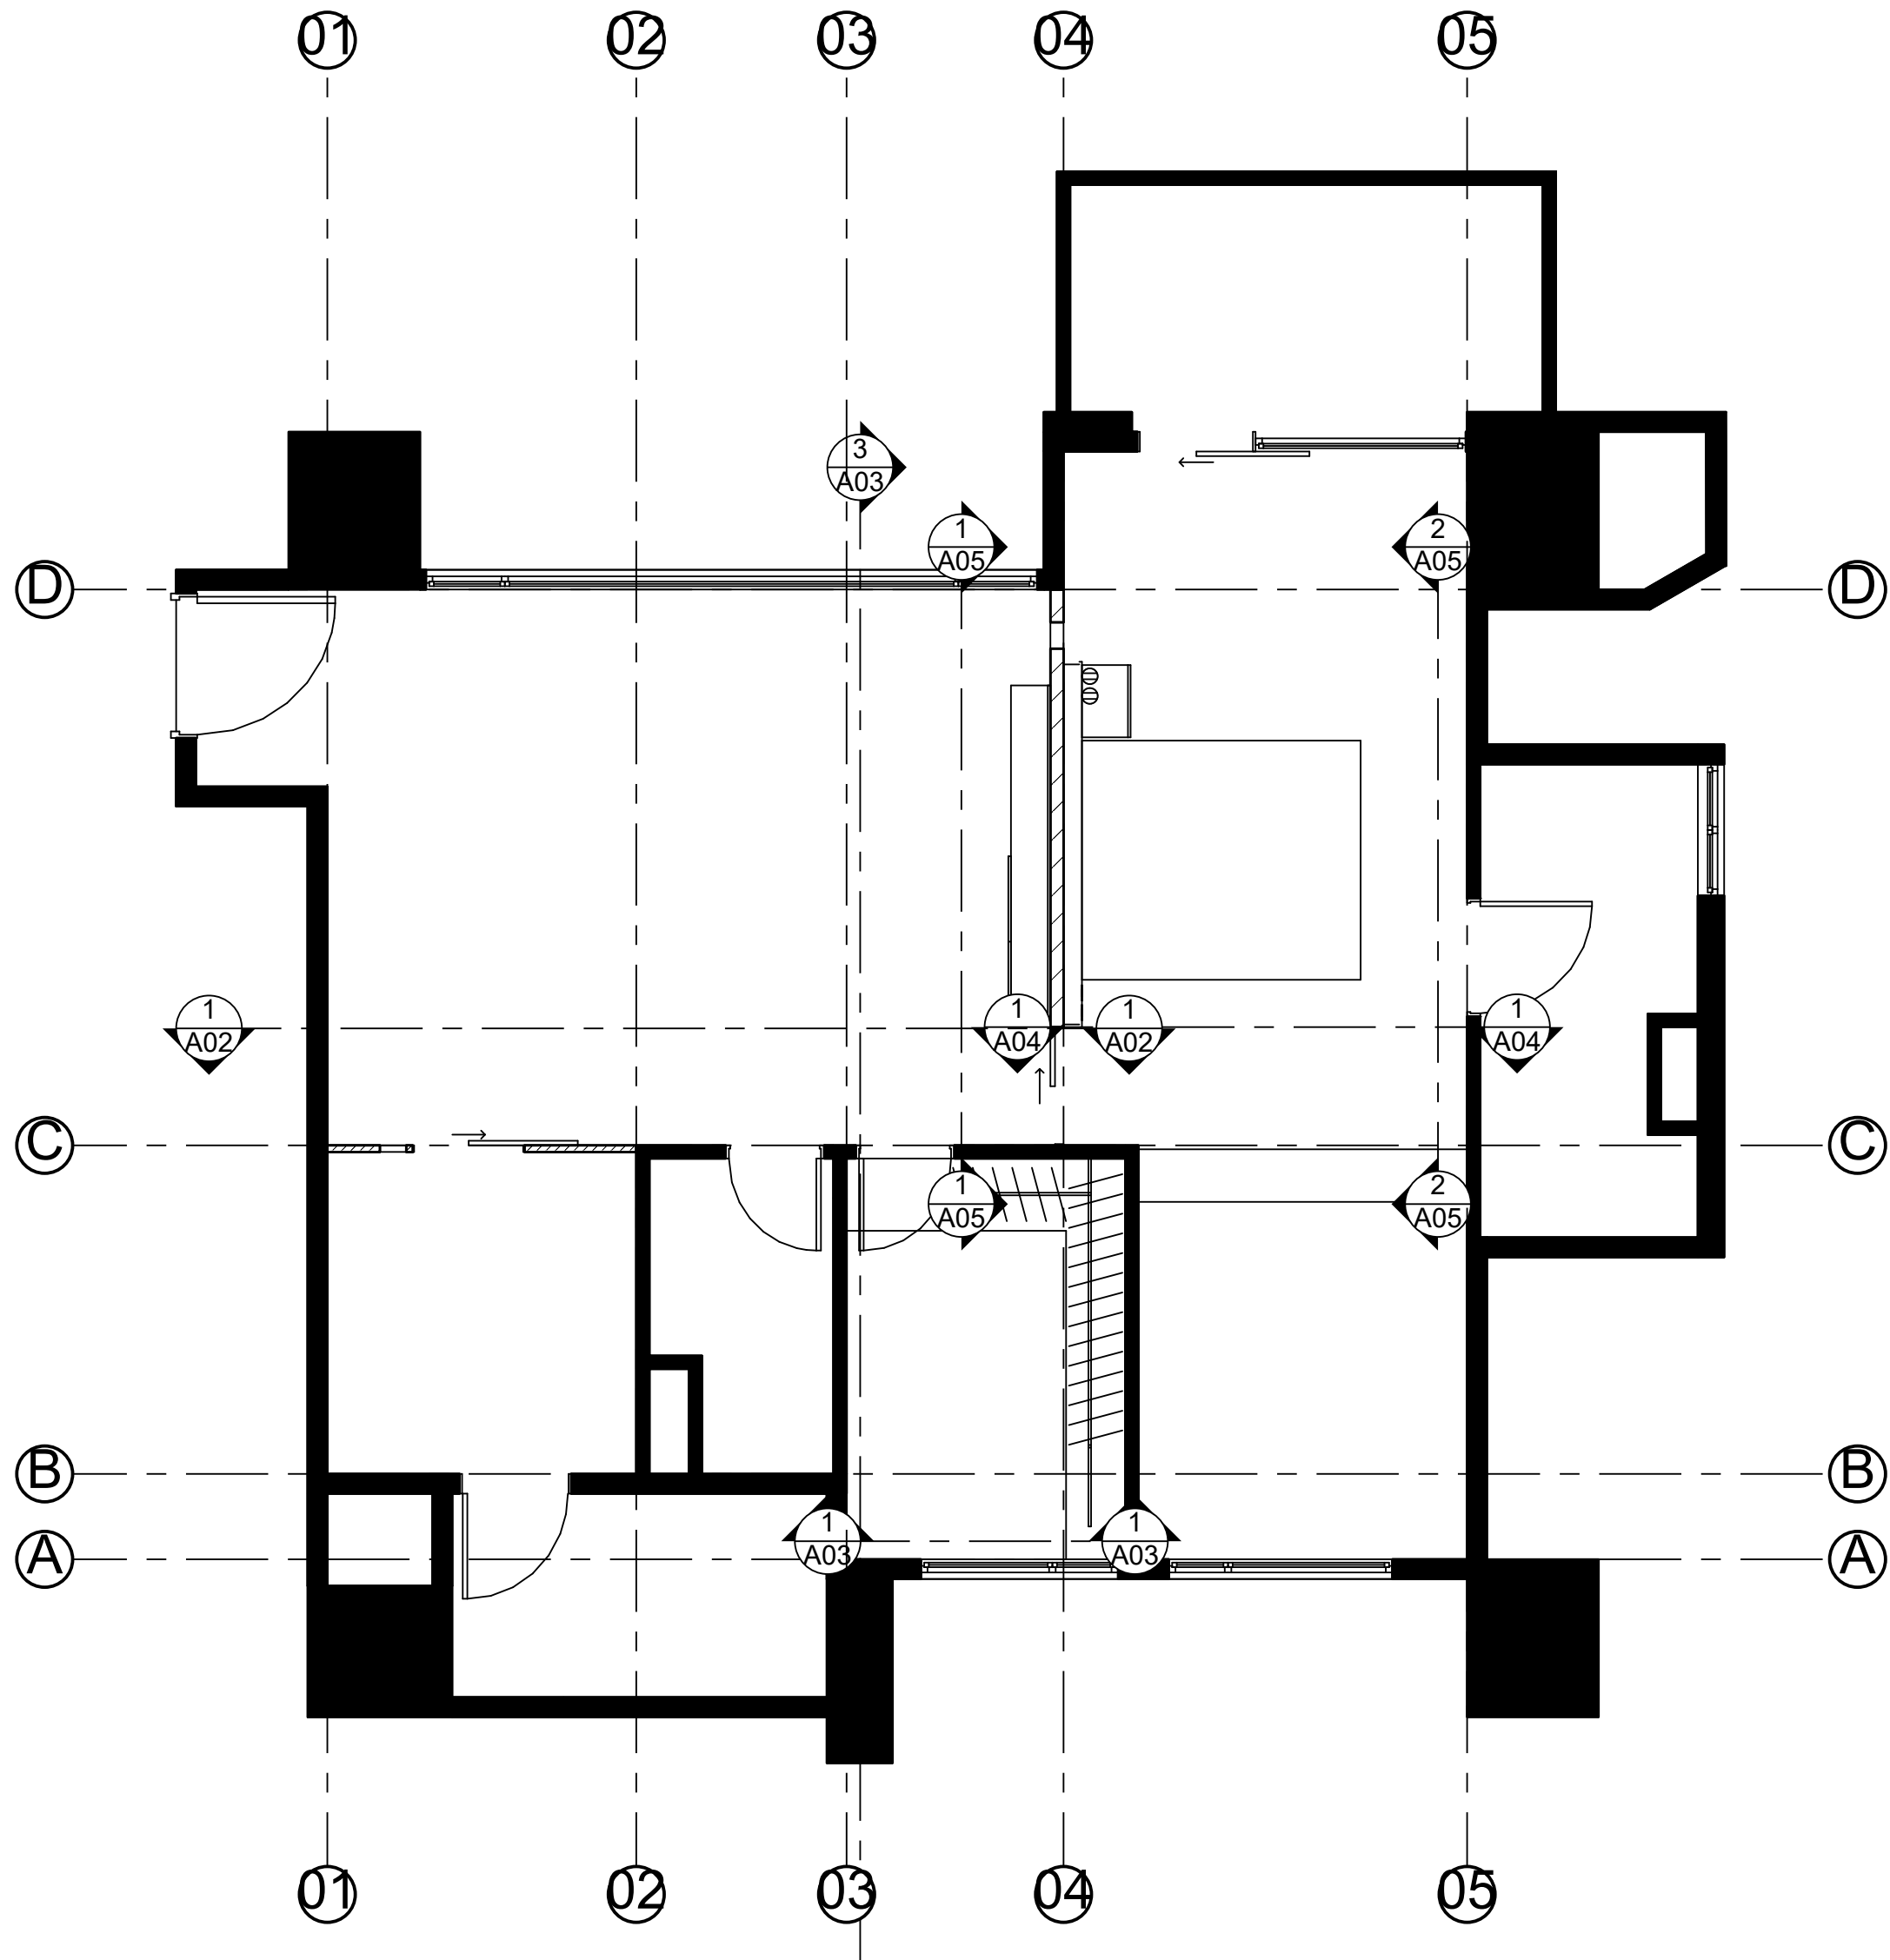

1 FLOOR PLAN
1:50


REV. NO.	DESCRIPTION	AUTHOR	ISSUED	DATE	NOTES
					DO NOT SCALE DRAWINGS

COMPANY	GRID NORTH
DRAWING TITLE	
FLOOR	
DRAWING NUMBER	REV
A01	None

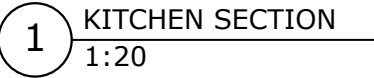


REV. NO.	DESCRIPTION	AUTHOR	ISSUED	DATE	NOTES
					DO NOT SCALE DRAWINGS


COMPANY		GRID NORTH	
			
DRAWING TITLE			
KITCHEN			
DRAWING NUMBER		REV	
A02		None	

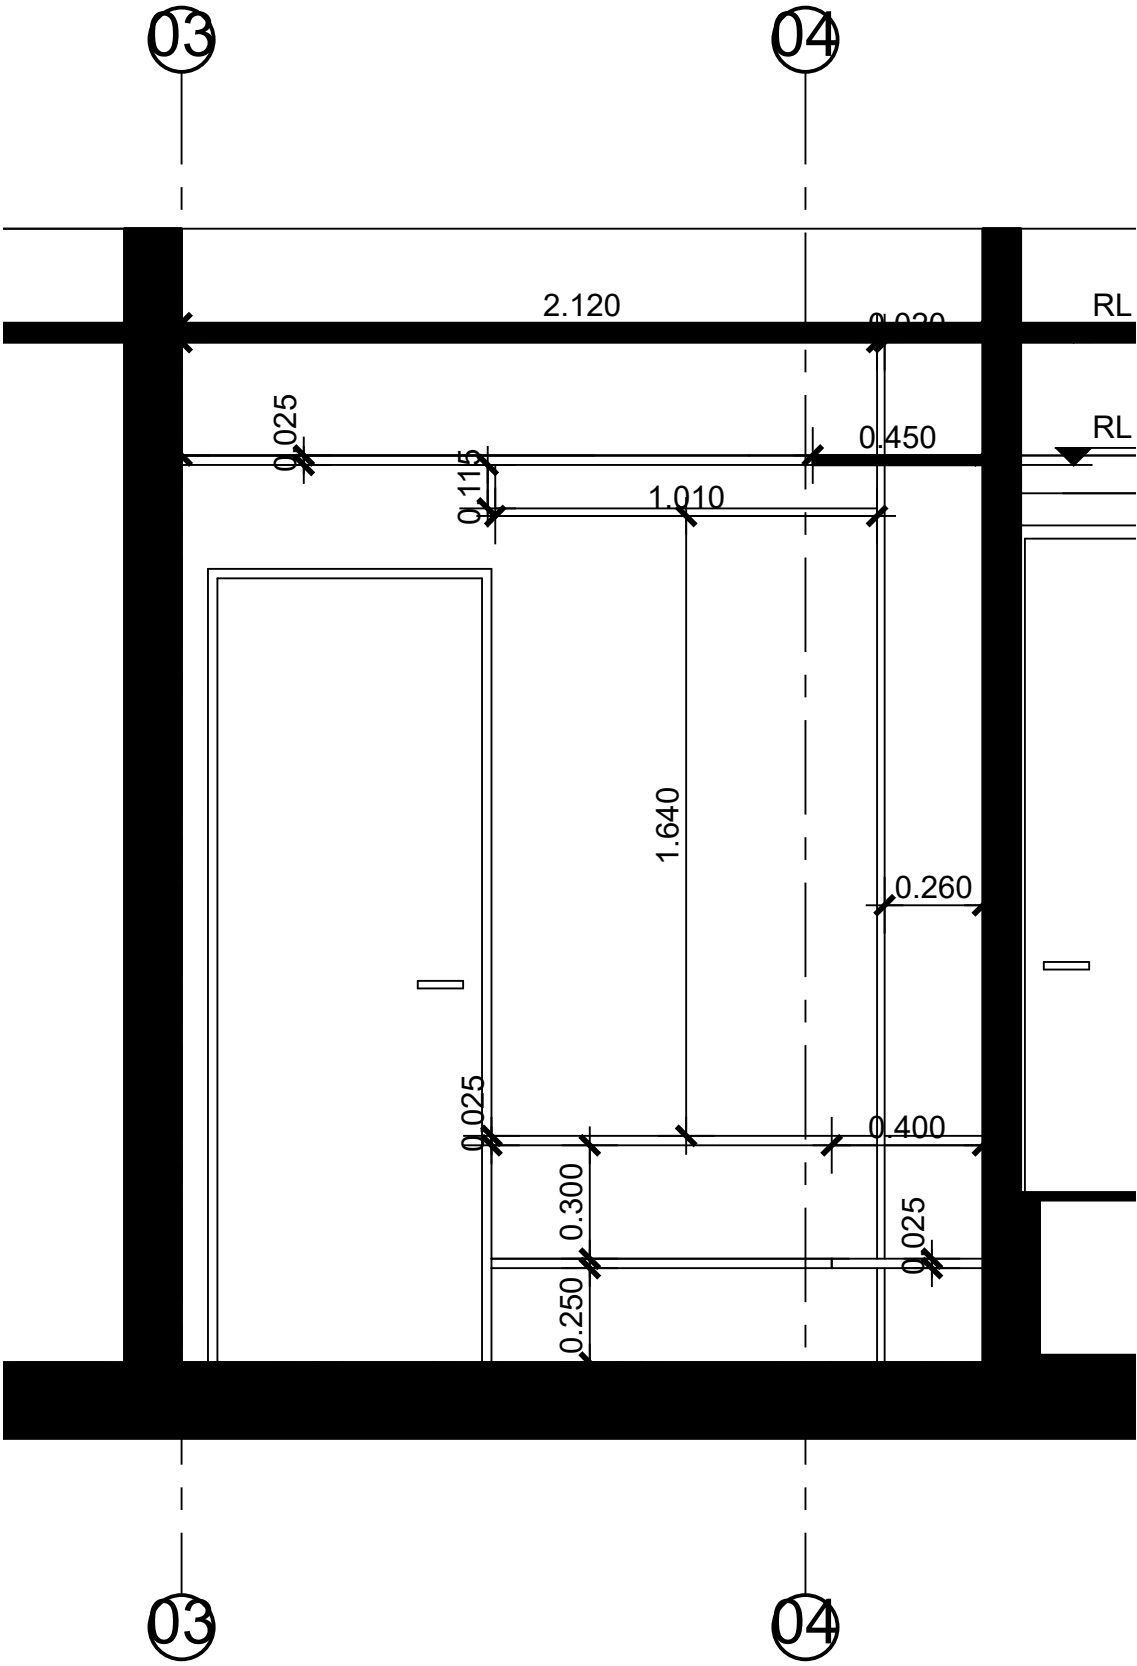

1 WARDROBE SECTION
1:20

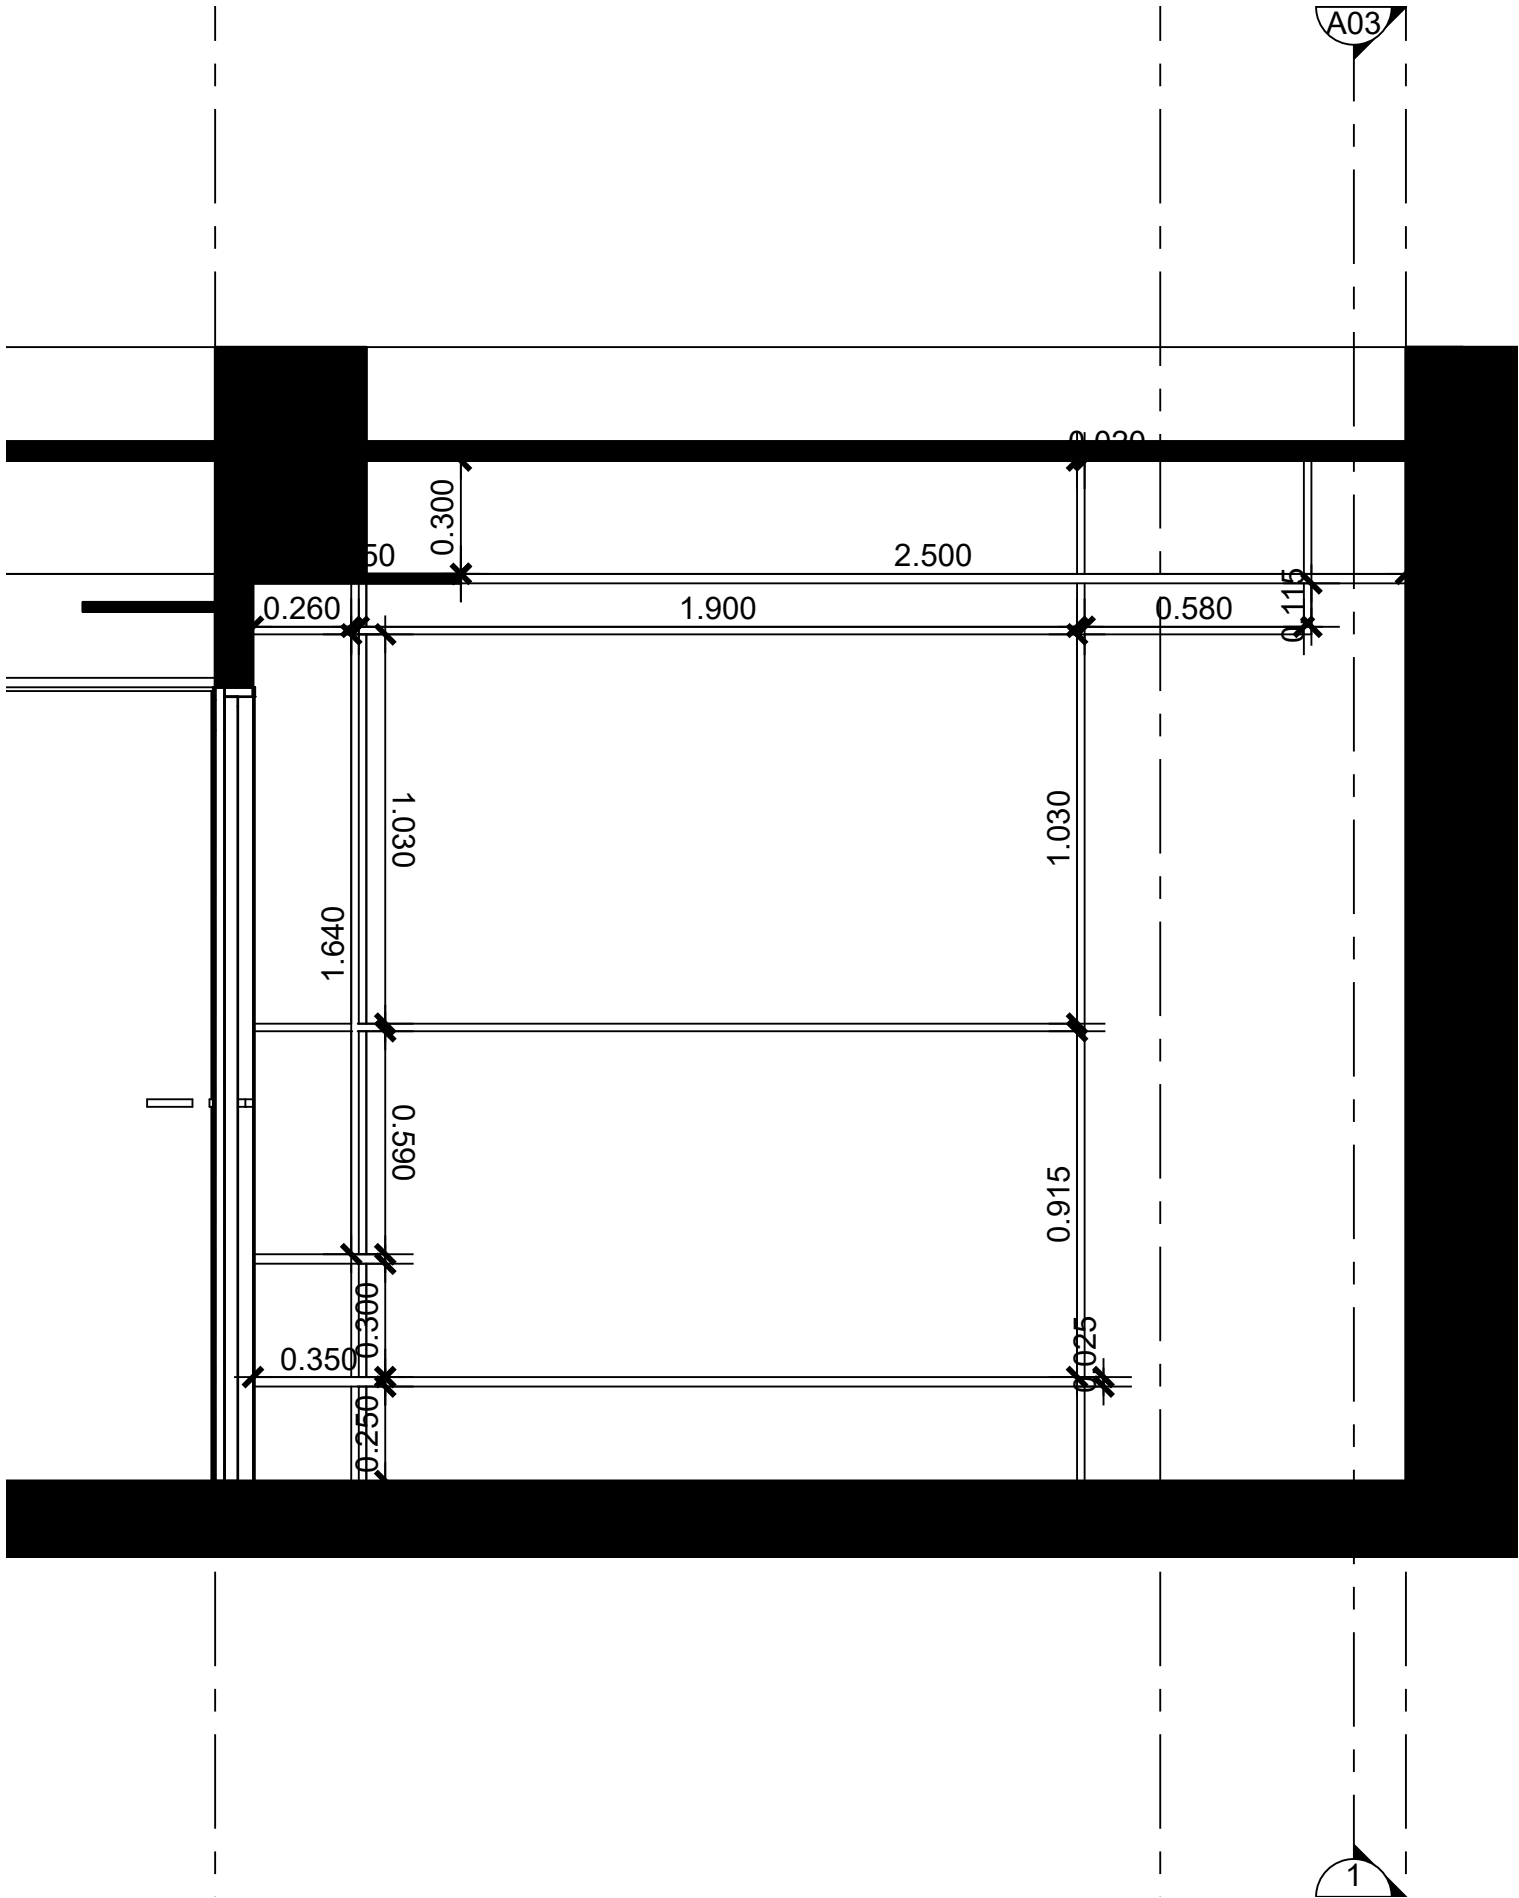


3 WARDROBE SECTION
1:20

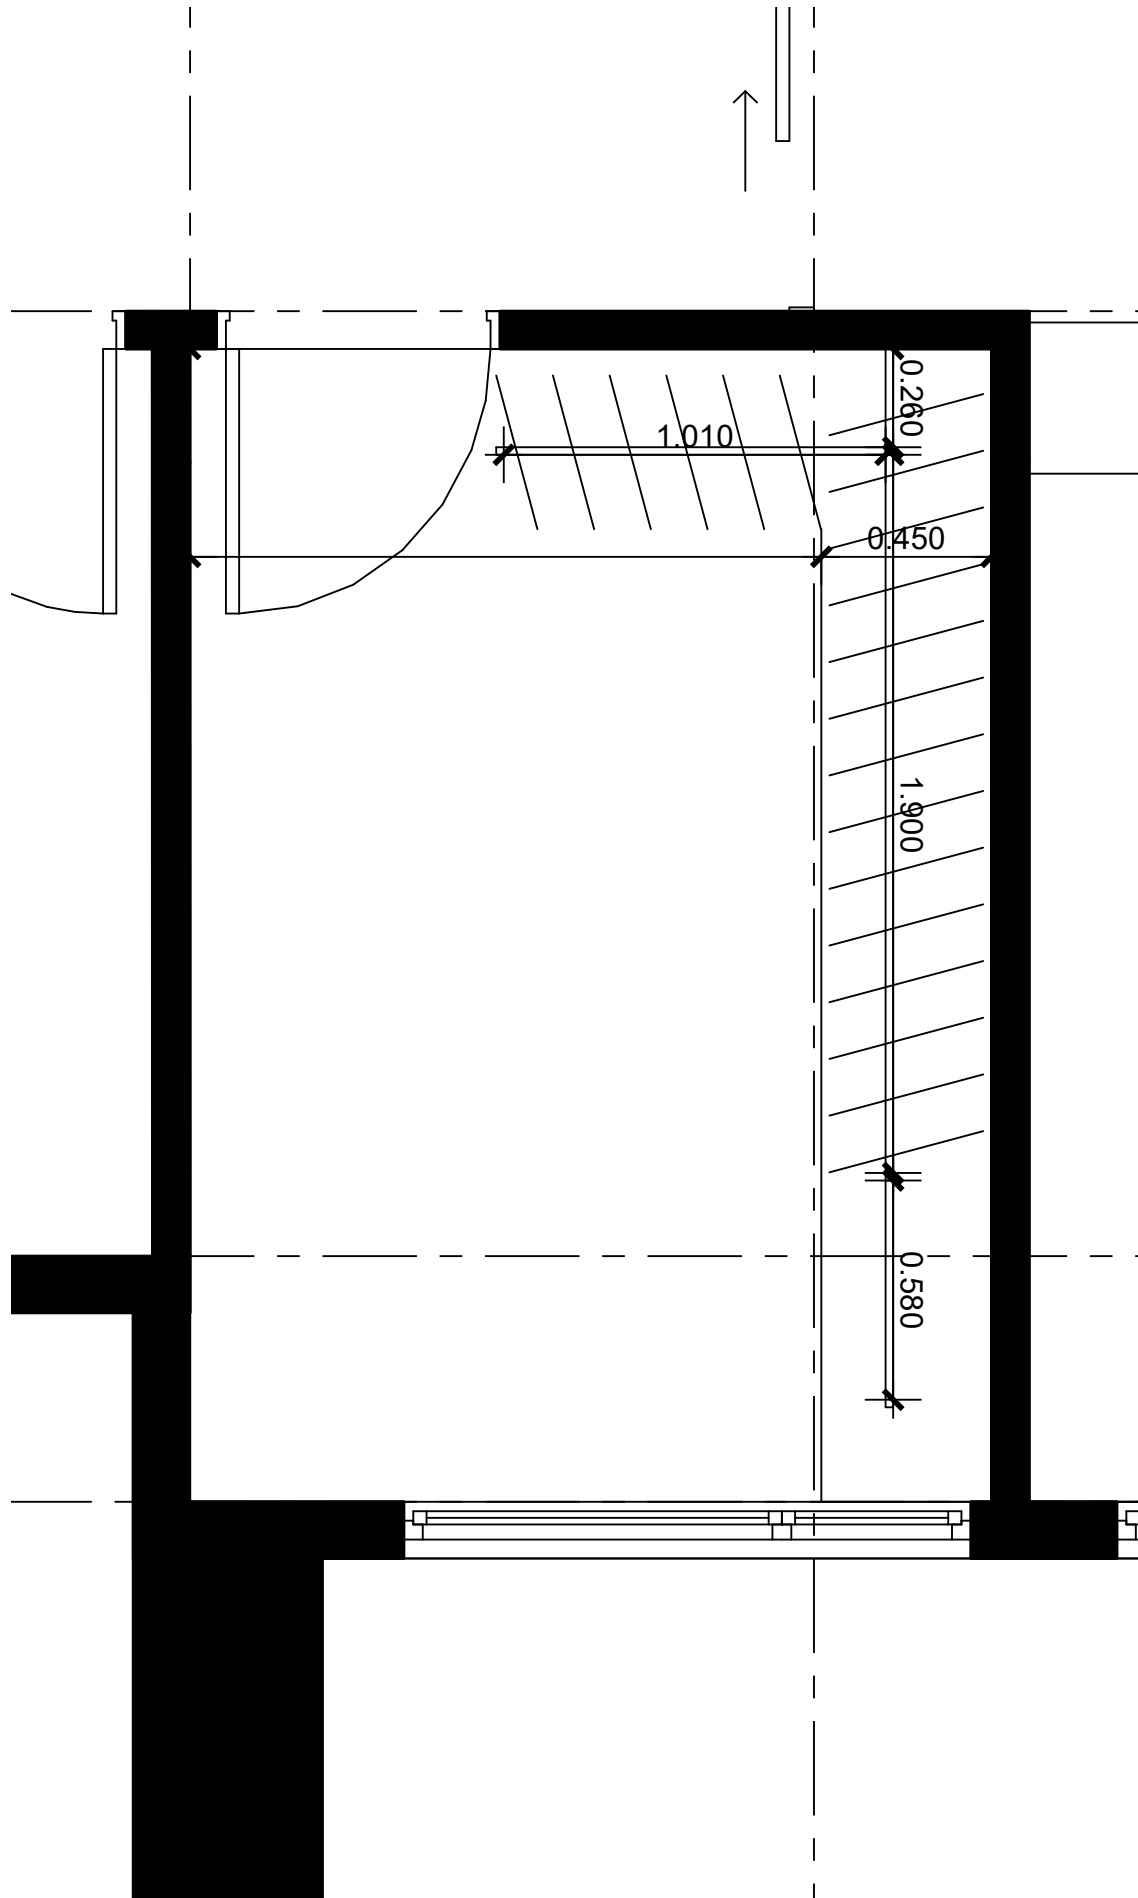


2 TOP WARDROBE
1:20

REV. NO.	DESCRIPTION	AUTHOR	ISSUED	DATE	NOTES
					DO NOT SCALE DRAWINGS

COMPANY	GRID NORTH
DRAWING TITLE WARDROBE	REV None
DRAWING NUMBER A03	

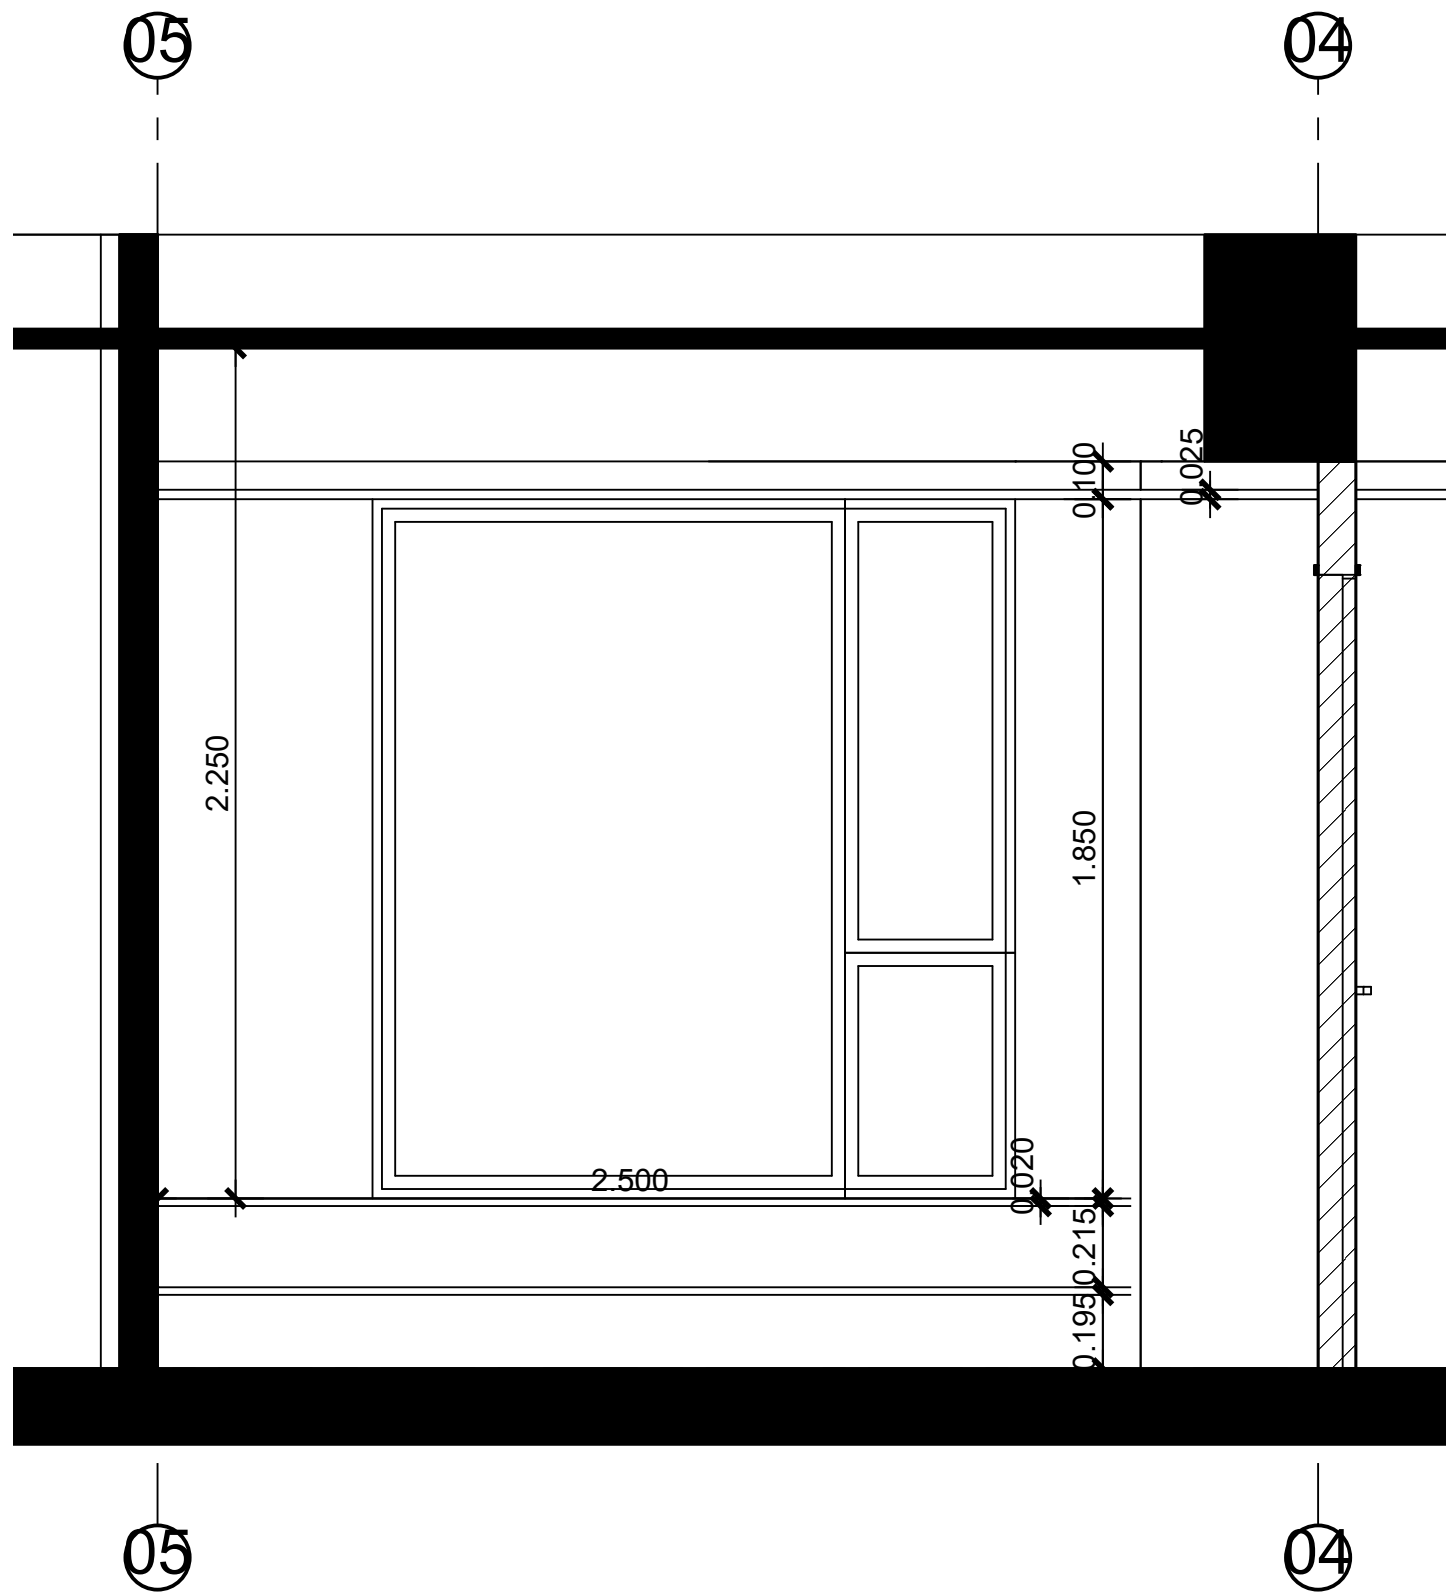

1 WASHITSU SECTION
1:20

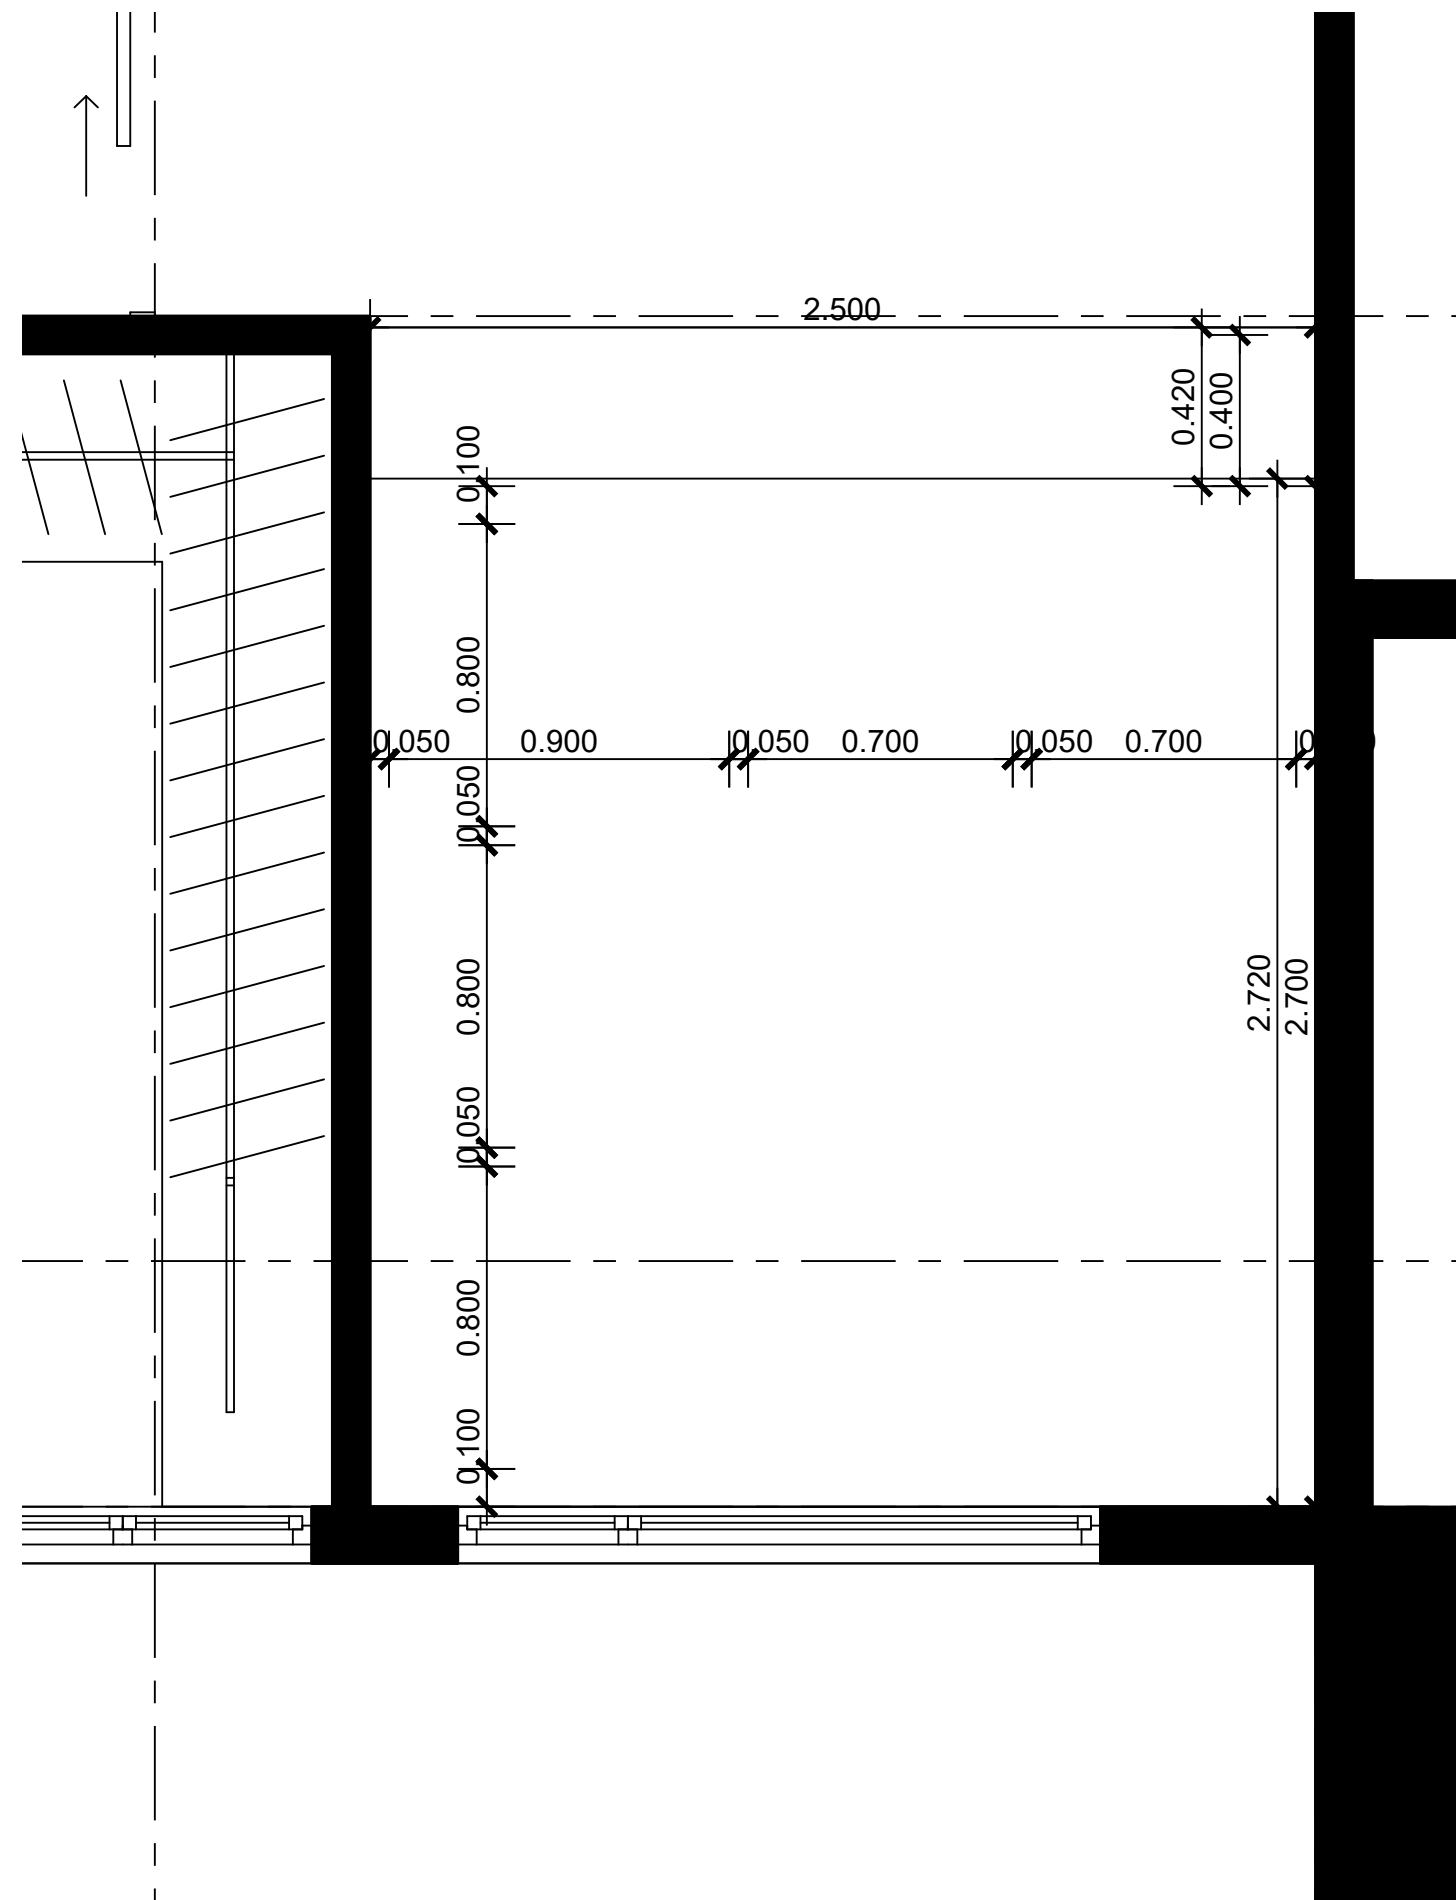


2 TOP WASHITSU
1:20

REV. NO.	DESCRIPTION	AUTHOR	ISSUED	DATE	NOTES
					DO NOT SCALE DRAWINGS

COMPANY	GRID NORTH
DRAWING TITLE WASHITSU	
DRAWING NUMBER A04	REV None


3 TOP BED
1:20

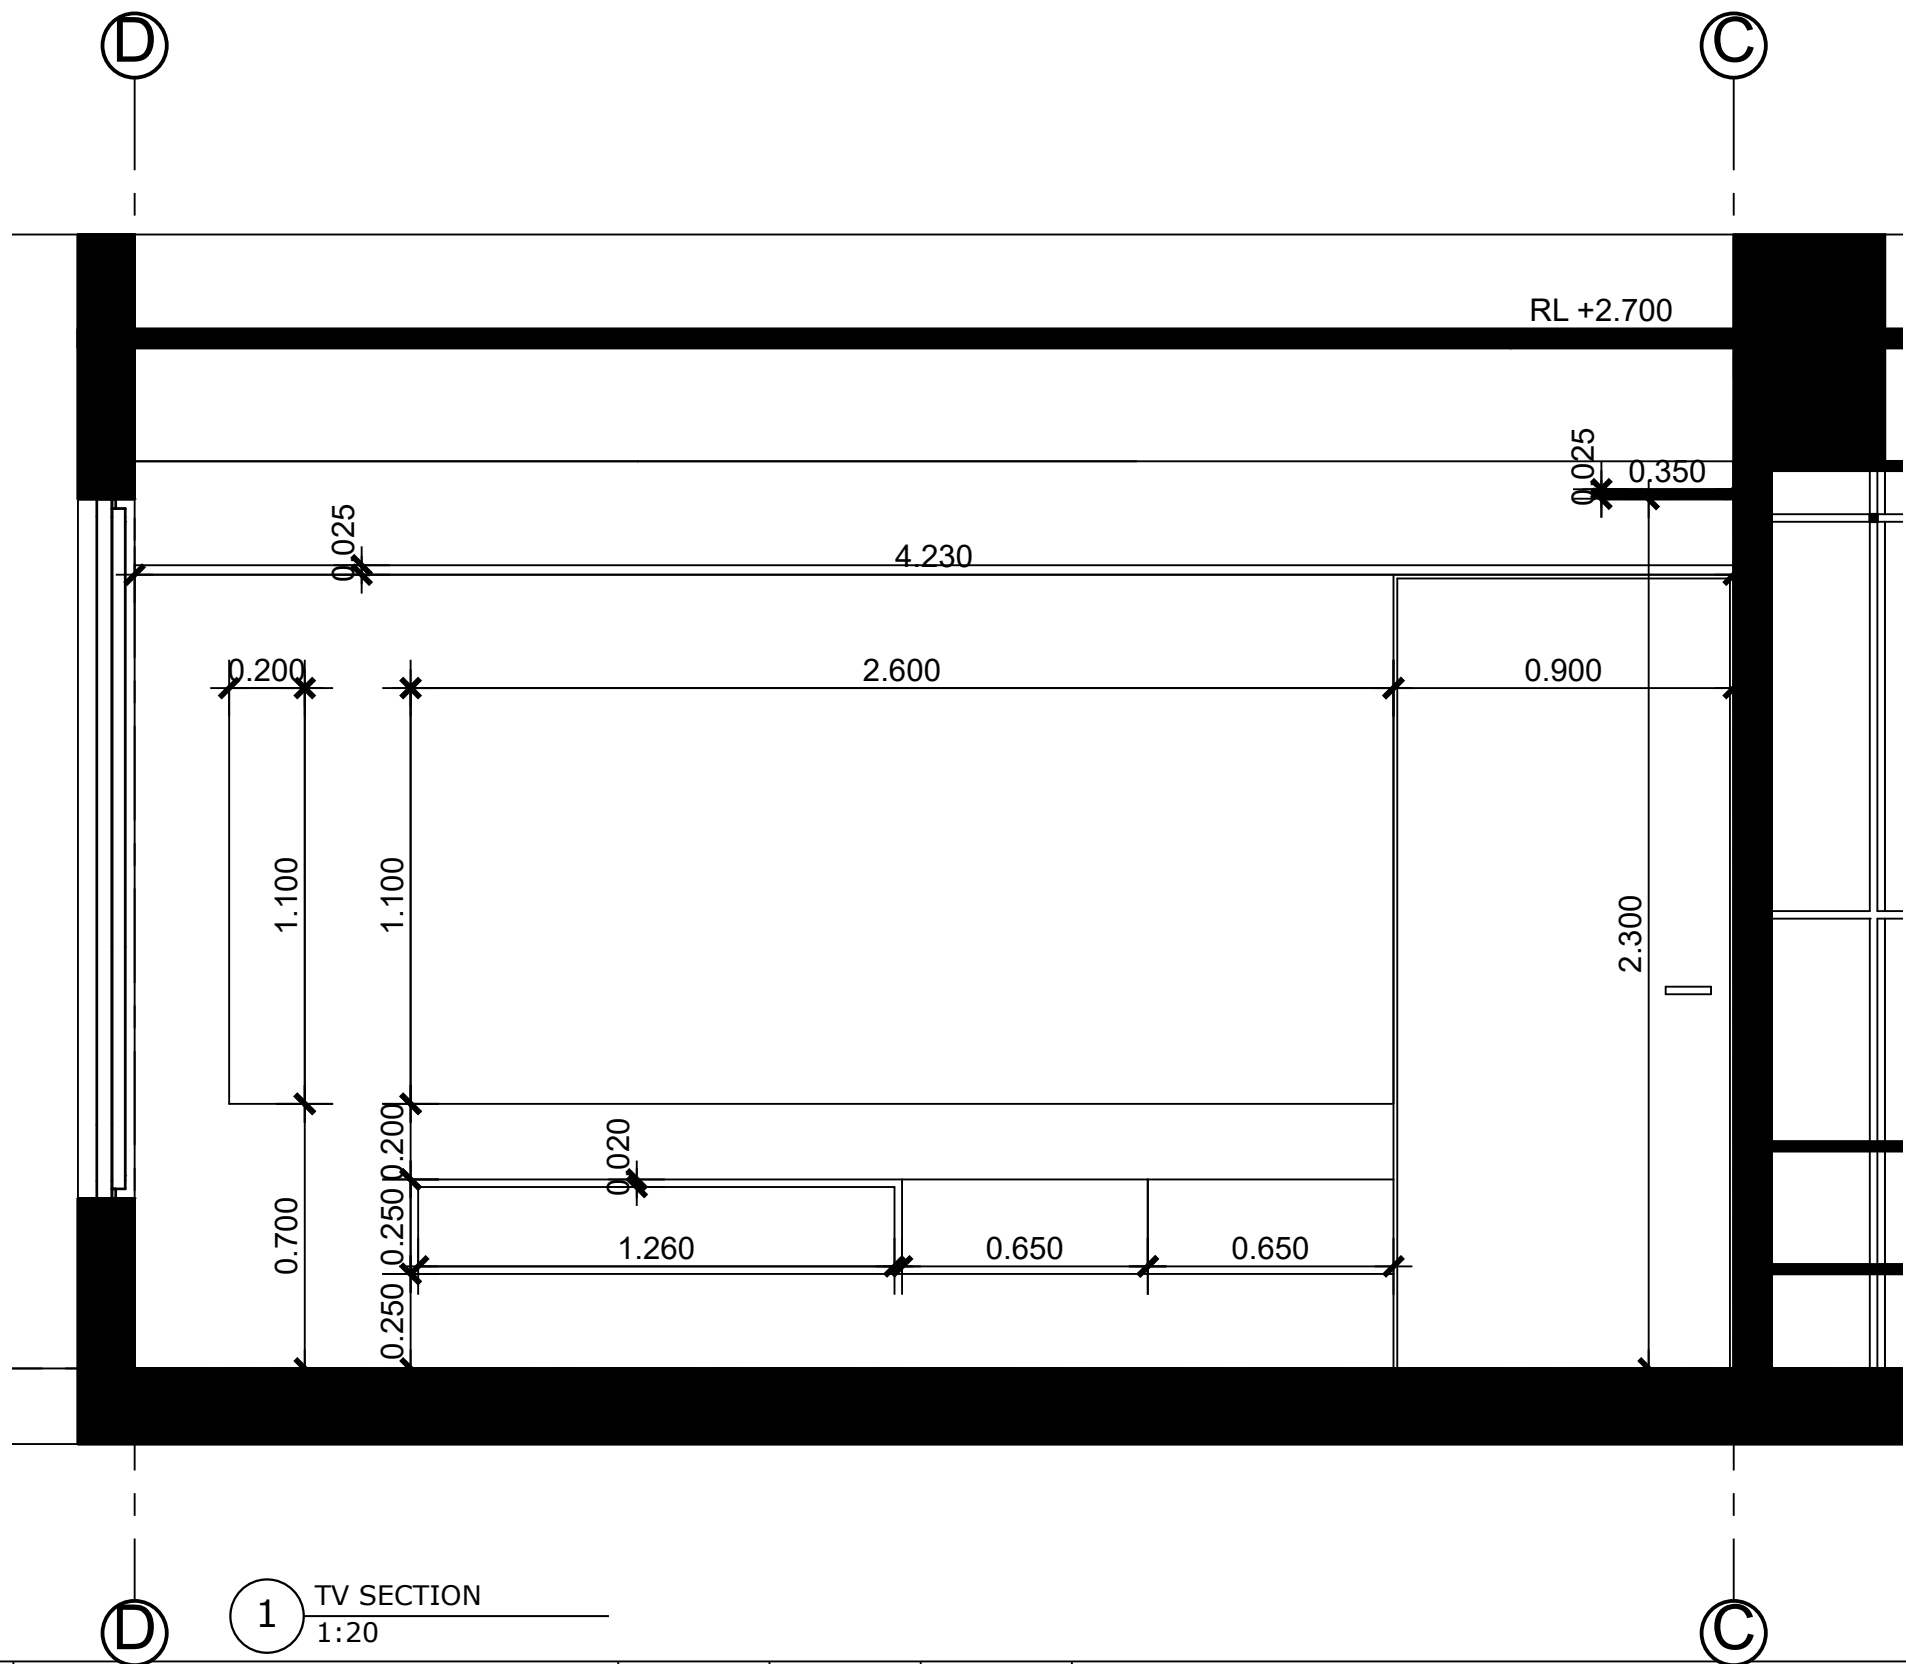

1 TV SECTION
1:20

REV. NO.	DESCRIPTION	AUTHOR	ISSUED	DATE	NOTES
					DO NOT SCALE DRAWINGS

2 BED SECTION
1:20

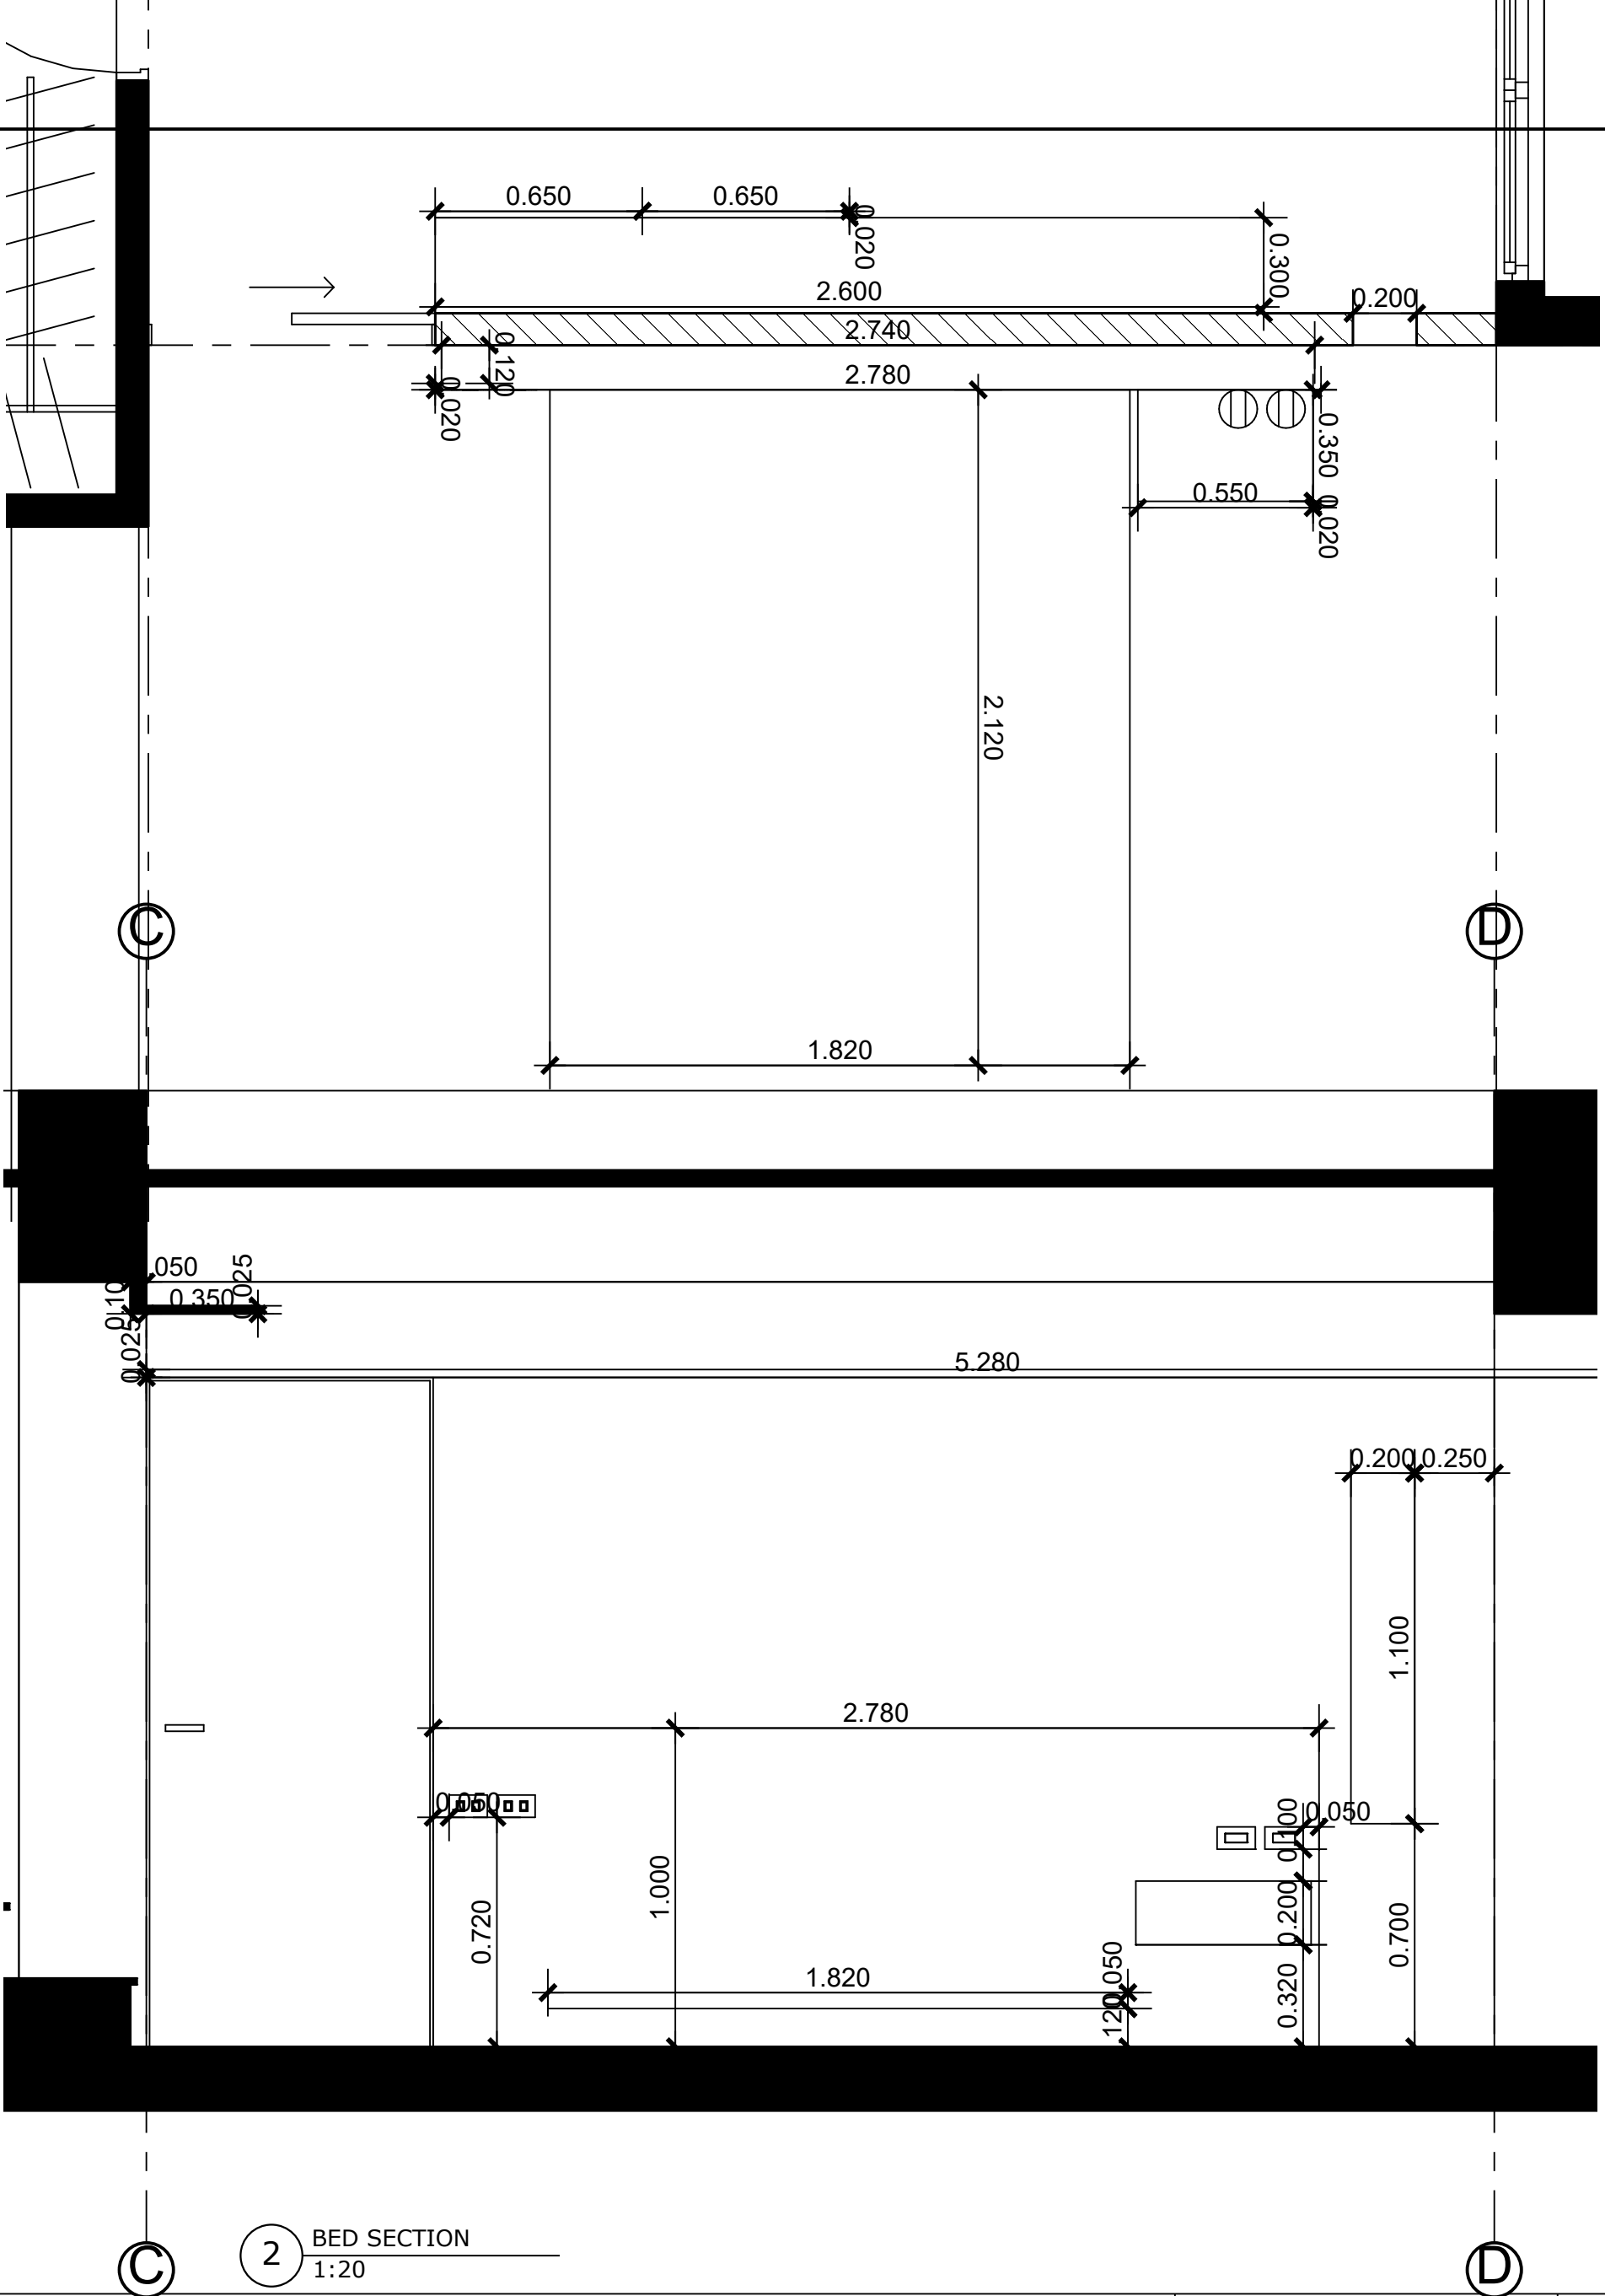

COMPANY	GRID NORTH
DRAWING TITLE	TV
DRAWING NUMBER	A05
REV	None